

✎
 건축개요

구 분	내 용					비 고
대 지 위 치	인천광역시 서구 당하동 1250번지 (검단신도시 P2-주9)					
지 역 지 구	준주거지역 / 지구단위계획구역					
대 지 면 적	지번	지적면적	제외면적	도로제척면적	신청면적	
	1250	2,311.20 m²	- m²	- m²	2,311.20 m²	
지 목	주차장					
도 로	13M / 13M / 13M 도로에 각각 33.32M / 60.95M / 45.12M 접합					
공 사 종 류	신축					
주 용 도	자동차관련시설-주차장(주차전용건축물)					
건 축 규 모	지하1층 / 지상 5층					법정 : 5층 이하
주 구 조	철근콘크리트 구조 - 라멘조					
최 고 높 이	23.94 M					
건 축 면 적	1,848.14 m²					
연 면 적	8,648.12 m²					
용적률산정연면적	8,405.47 m²					
건 폐 율	1,848.14 / 2,311.20 X 100 = 79.96 %					법정 : 80 %
용 적 률	8,405.47 / 2,311.20 X 100 = 363.68 %					법정 : 400 %
주 차 계 획	법 정	-				
	계 획	139 대 -(전기자동차 주차구역 7대 포함)				
조 경 계 획	법 정	해당없음				법정 : - %
	계 획	399.66 m² (지상 :29.94 m² + 옥상 : 369.72m²)				계획 : 17.27 %
저 수 조	-					
정 화 조	하수종말처리장 연결					

비 고

- 근린생활시설 등의 배치기준

- 주차장으로 사용되는 부분의 비율이 건축연면적의 70% 이상
--->72.31 % 적용
- 근린생활시설 등의 비율은 지상층 연면적에 대한 대지면적 비율(용적률)의 30퍼센트 미만이어야 한다.
--->27.69 % 적용
- 근린생활시설 등을 설치할 경우 지상 1층부에는 바닥면적의 50퍼센트 이하로 하여야 한다.
--->49.77 % 적용

- 냉난방 면적 3,000m² 미만

- 에너지 절약계획서 제출대상 - (500m²이상)
- 인천광역시 녹색건축물 설계기준 "라" 등급 적용 - (연면적합계 5백m² 이상 ~ 3천m² 미만)
비주거 - 동별 연면적의 합계. 다만, 건축물의 에너지절약설계기준 (국토교통부 고시)에 따른 냉·난방 면적이 연면적의 50% 미만인 경우에는 냉·난방 면적의 합계를 적용
--->2,863.34 (냉난방면적) / 8,648.12 (연면적) x 100% = 33.11%

✎
 층별개요

구 분	층 별	용 도	면 적 (m²)						에너지절약 설계기준 냉난방면적	비 고
			근린생활시설	근린생활시설 공용면적	합 계	주차장	주차장 공용면적	합 계	층 합 계	
지하층	지하1층	기계실/방재실		67.24	67.24		175.41	175.41	242.65	
	소계			67.24	67.24		175.41	175.41	242.65	
지상층	1층	제1종근린생활시설 (소매점)	848.40	63.92	912.32	856.30	64.52	920.82	1,833.14	960.60
	2층	제2종근린생활시설 (일반음식점)	330.60	37.26	367.86	1,298.05	146.23	1,444.28	1,812.14	497.85
	3층	제2종근린생활시설 (학원)	330.60	37.26	367.86	1,298.05	146.23	1,444.28	1,812.14	497.85
	4층	제2종근린생활시설 (사무소)	330.60	37.26	367.86	1,298.05	146.23	1,444.28	1,812.14	497.85
	5층	제1종근린생활시설 (휴게음식점)	266.88	30.92	297.80	751.09	87.02	838.11	1,135.91	368.58
	옥탑층								16.24	면적 미산입
	소계		2,107.08	206.62	2,313.70	5,501.54	590.23	6,091.77	8,421.71	2,822.73
합 계			2,107.08	273.86	2,380.94	5,501.54	765.64	6,267.18	8,664.36	2,867.54

✎
 건축연면적에 대한 주차장 비율 (70%이상)

구 분	전용면적(m²)	공용면적(m²)	합 계(m²)	공급비율(%)	비 고
근린생활시설	2,107.08	286.71	2,393.79	27.69	주차장 비율 70%이상 -72.31% 적용
주차장	5,501.54	748.59	6,254.33	72.31	
합 계	7,608.62	1,035.30	8,648.12	100.00	

✎
 용적률에 대한 근린생활시설 비율 (30%미만)-지하층 제외

구 분	전용면적(m²)	공용면적(m²)	합 계(m²)	공급비율(%)	비 고
근린생활시설(1~5층)	2,107.08	220.67	2,327.75	27.69	용적률의 30%미만 -27.69% 적용
주차장(1~5층)	5,501.54	576.18	6,077.72	72.31	
합 계	7,608.62	796.85	8,405.47	100.00	

✎
 1층 바닥면적에 대한 근린생활시설 비율 (50%이하)

구 분	전용면적(m²)	공용면적(m²)	합 계(m²)	공급비율(%)	비 고
근린생활시설(1층)	848.40	63.92	912.32	49.74	1층근린생활시설 면적비율 50% 이하 적용. -49.77% 적용
주차장(1층)	856.30	64.52	920.82	50.26	
합 계	1,704.70	128.44	1833.14	100.00	

공 사 명
PROJECT TITLE

인천광역시 서구
당하동 1250번지
주차전용건축물
신축공사

주 기
NOTE

△				
△				
△				
△				
△				
△				
No.	Date	Revision	Description	Chkd.

(주)해인건축사사무소

HAEIN ARCHITECTURE

E-mail : ar5585@naver.com
TEL.031)987-5585, FAX.031)985-5585

도면명 TITLE

설계개요

축 적 SCALE	A1	1 / NONE
	A3	1 / NONE

일 자
DATE

설 계
ARCHTECT


달 당
DRAW.

검 토
CHECK

승 인
APPROVED

도면번호
DRAWING NO

A - 101

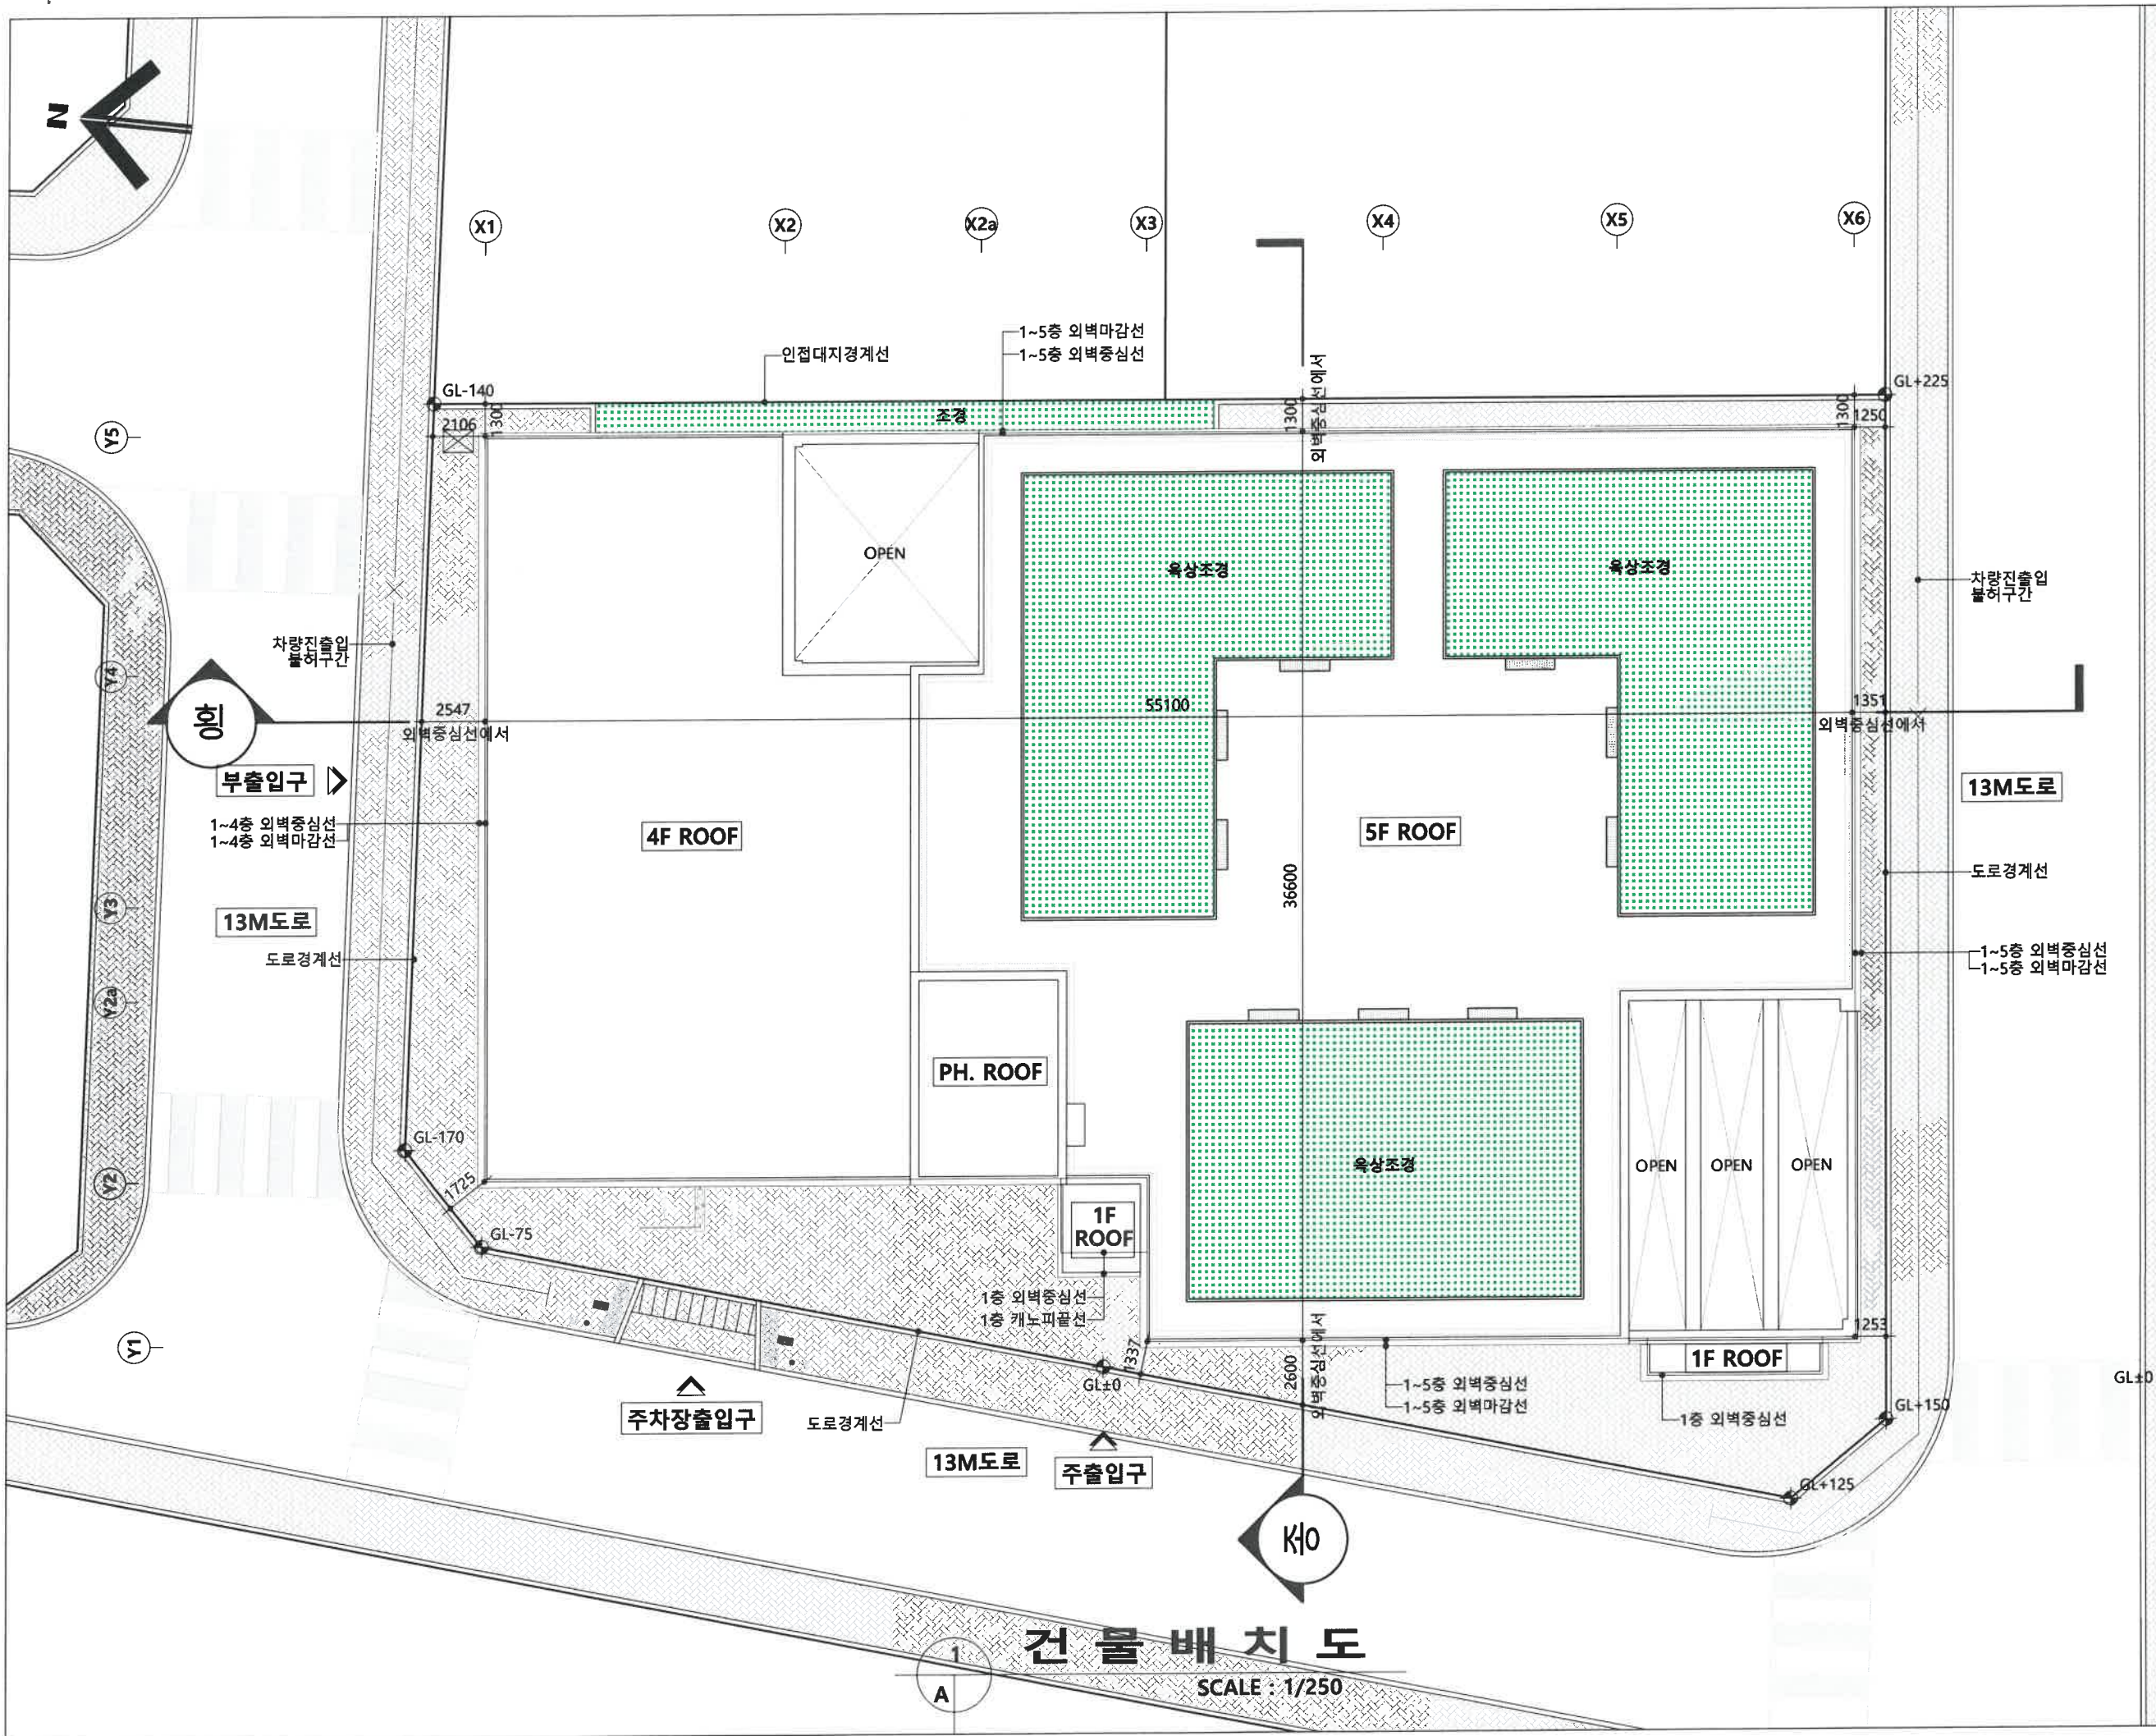

공사명
PROJECT TITLE

인천광역시 서구
당하동 1250번지
주차전용건축물
신축공사

주 기
NOTE

△			
△			
△			
△			
△			
△			

No.	Date	Revision Description	Chkd.
-----	------	----------------------	-------

(주)해인건축사사무소
HAEIN ARCHITECTURE

E-mail : sr5585@naver.com
TEL 031)987-5585, FAX 031)985-5585

도면명 TITLE

건물 배치도

축척 SCALE	A1	1 / 125
	A3	1 / 250

일 자
DATE

설 계
ARCHITECT

담 당
DRAW.

검 토
CHECK

승 인
APPROVED



도면번호
DRAWING NO

A - 102



SCALE : 1/250

A - 201

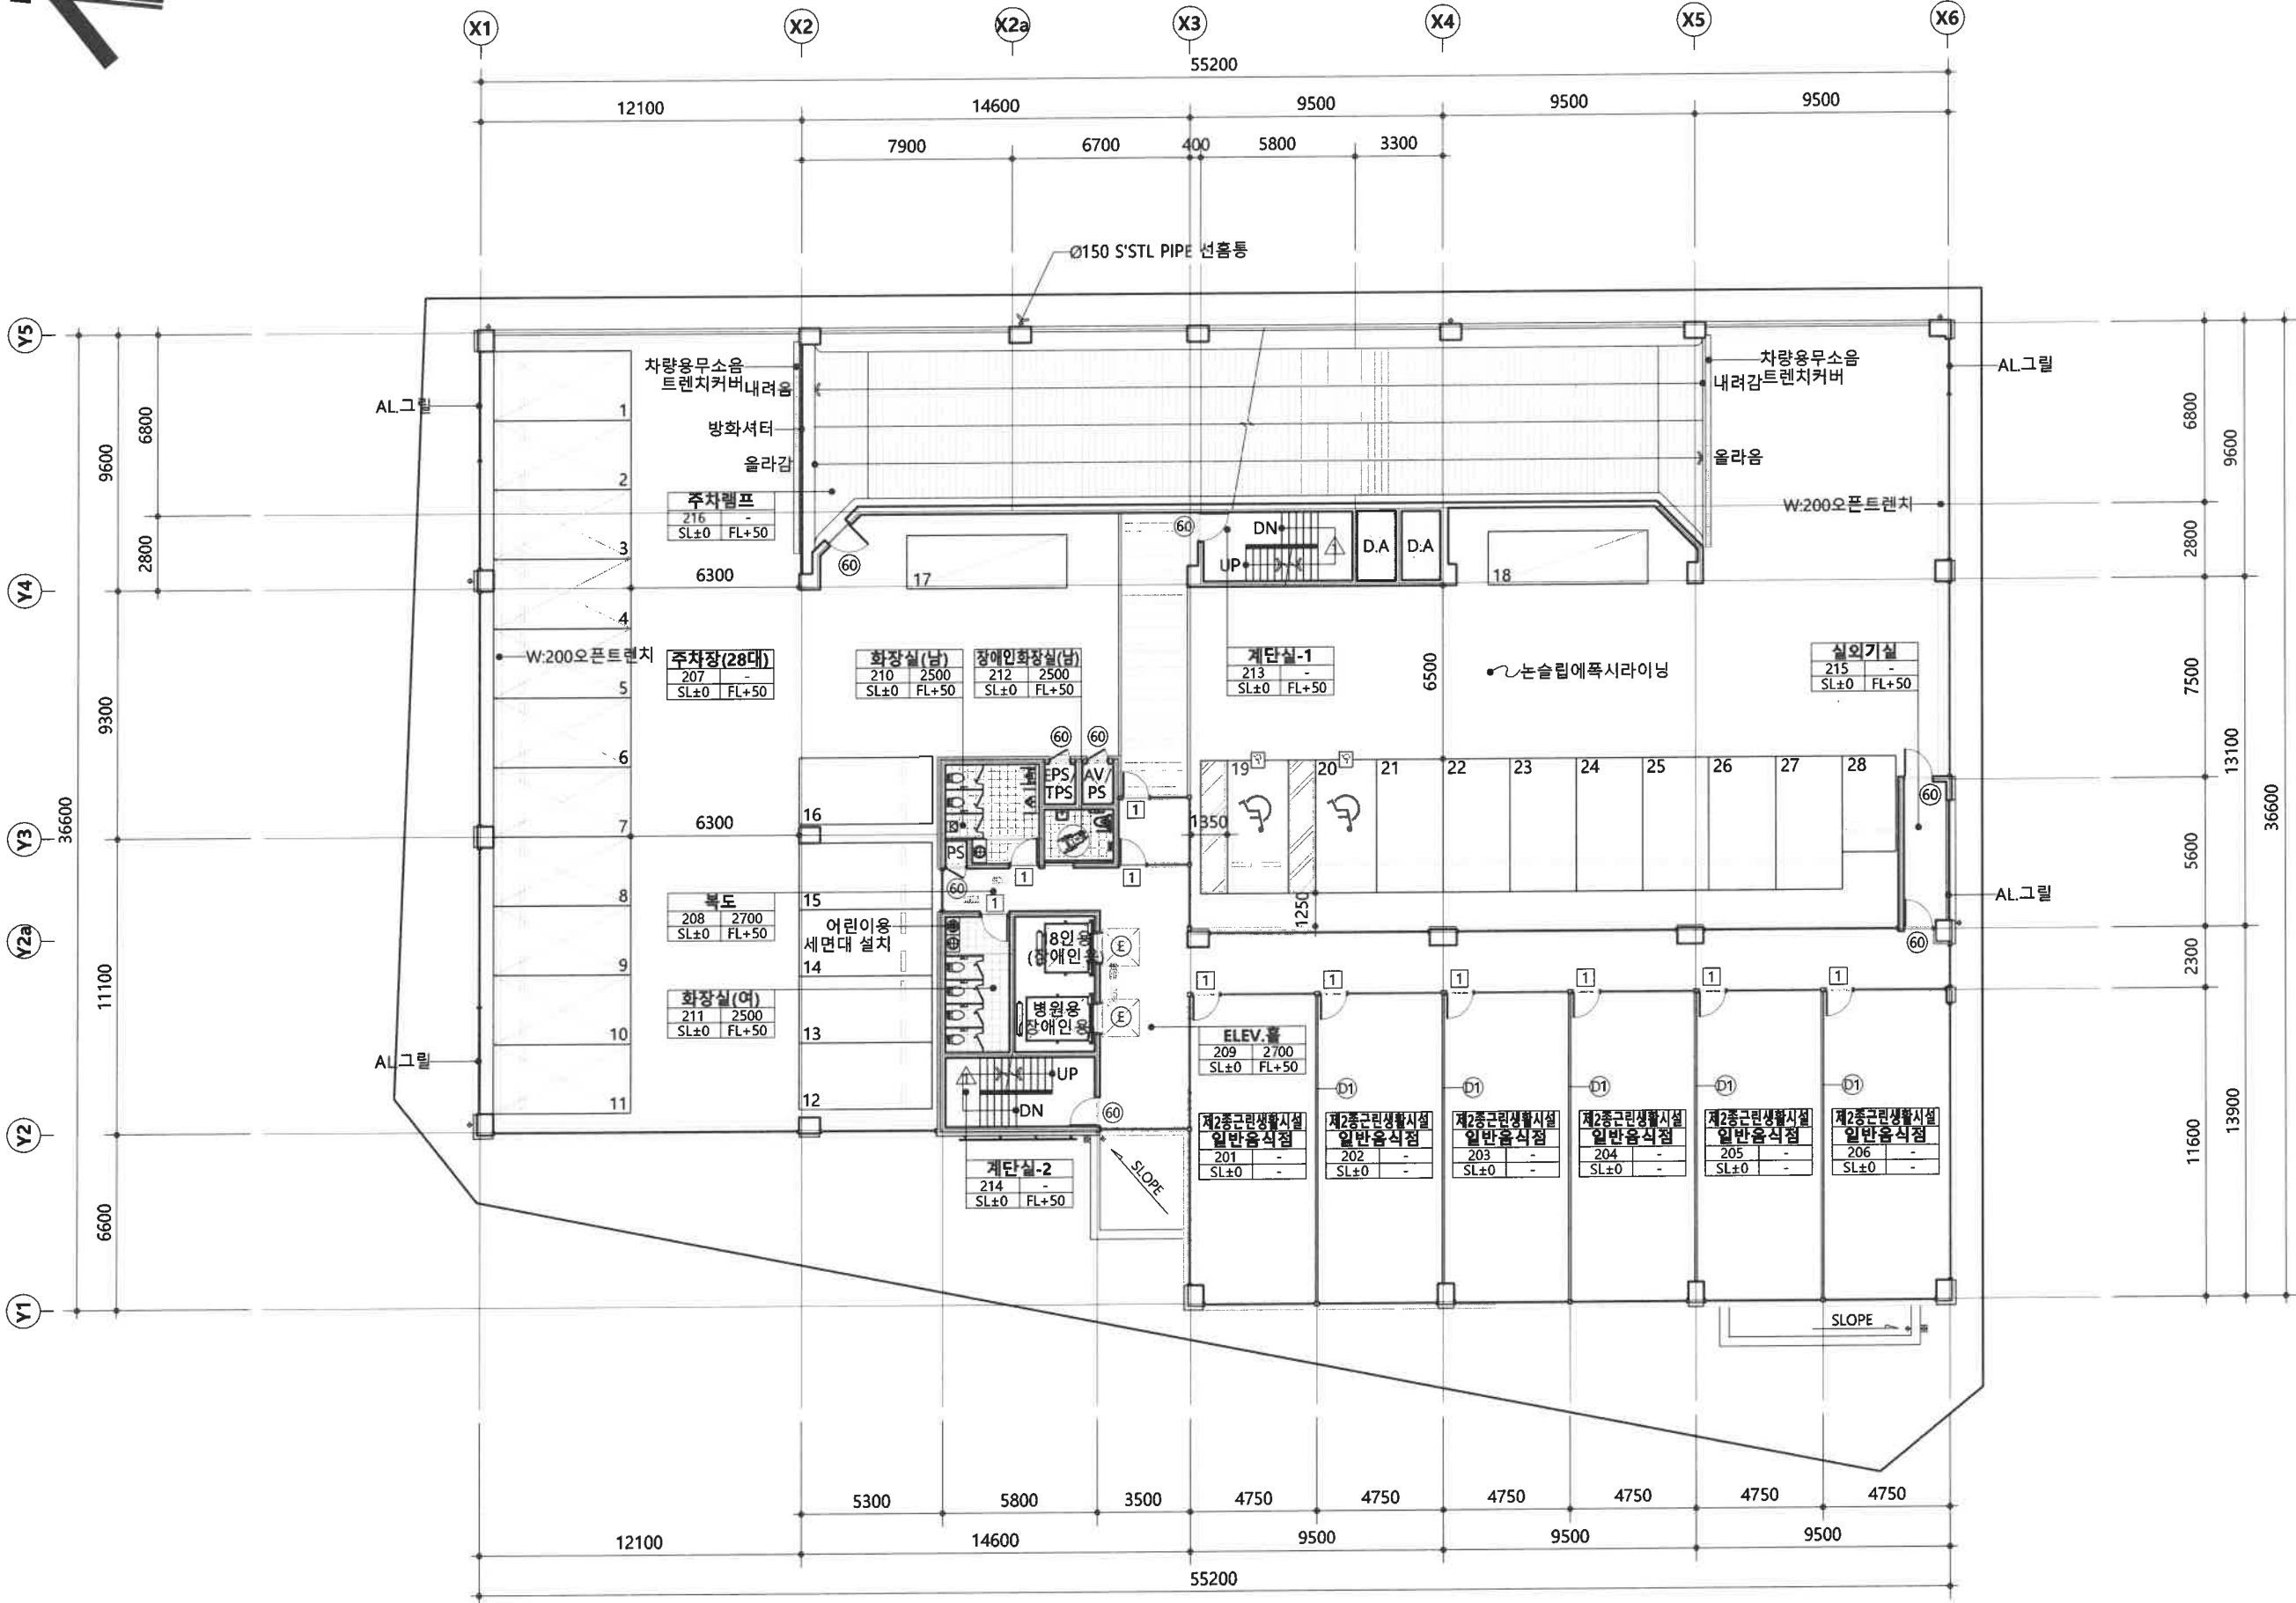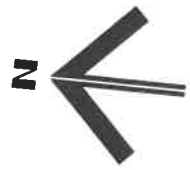

1
A

2 층 평 면 도

SCALE : 1/250

공 사 명
PROJECT TITLE

인천광역시 서구
당하동 1250번지
주차전용건축물
신축공사

주 기
NOTE

1. □:재료분리대
1:T-1.2 스테인레스(꼭=문쪽)
2. △:핸드레일
1:Ø38 S'ST PIPE 손잡이 난간
2:10X60 평철난간
3. ○:벽체리스트
D1: THK9.5 석고보드 2겹(양면)
(KS50x45x0.5T C-STUD)
4. 조적조에 문,창 설치시 인방설치
(인방높이는 OPEN쪽 1,800이상은
H-300, 1,800미만은 H-200 혹은
조적목과 동일)
5. 보크기, 스라브두께, 벽두께,
OPENING 등은 구조도면을
우선으로한다.
6. 실명
실번호 전정고
SL레벨 FL레벨
7. 60: 60분 방화문
8. ㉔: 승강기용 방화문

△				
△				
△				
△				
△				
△				

No.	Date	Revision	Description	Chkd.
-----	------	----------	-------------	-------

(주)해인건축사사무소
HAEIN ARCHITECTURE

E-mail : sr5585@naver.com
TEL:031)987-5585, FAX:031)985-5585

도면명 TITLE

2 층 평 면 도

축 치 SCALE	A1	1 / 125
	A3	1 / 250

일 자
DATE

설 계
ARCHITECT



담 당
DRAW.

검 토
CHECK

승 인
APPROVED

도면번호
DRAWING NO

A - 203

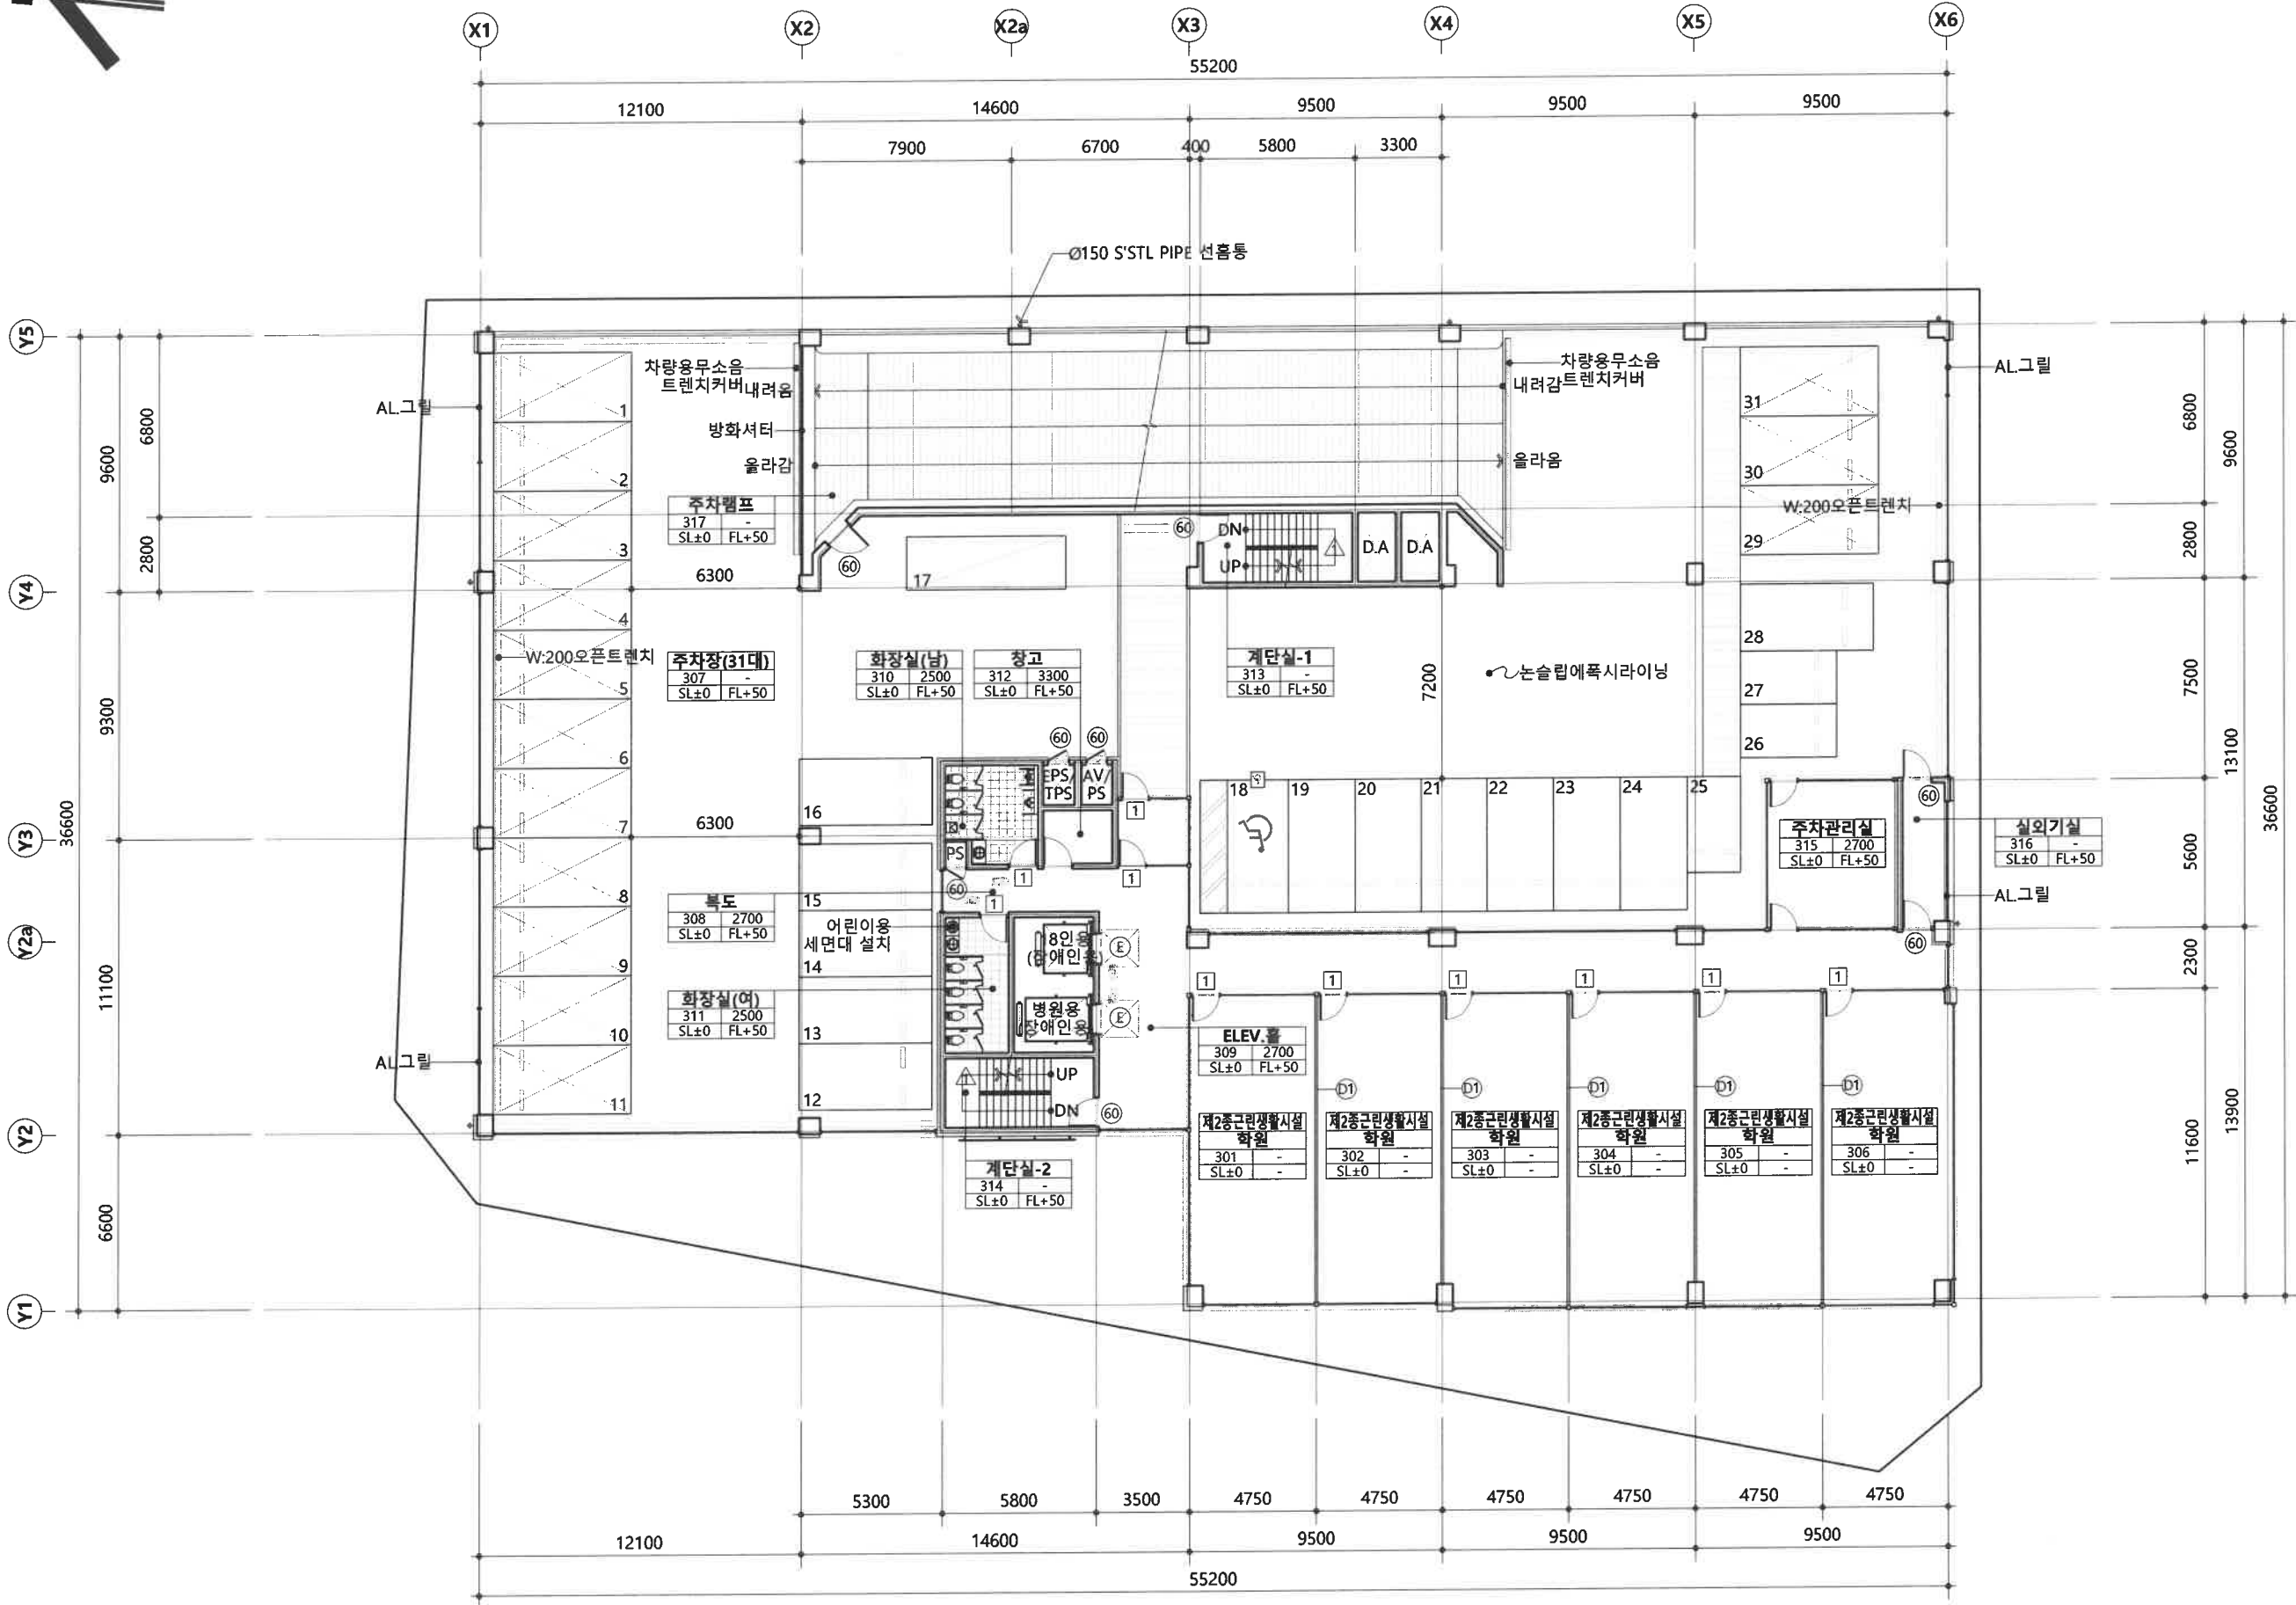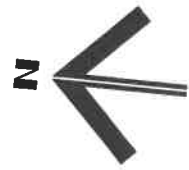

1
A

3 층 평 면 도

SCALE : 1/250

공 사 명
PROJECT TITLE

인천광역시 서구
당하동 1250번지
주차전용건축물
신축공사

주 기
NOTE

1. □: 재료분리대
1: T-12 스테인레스(꼭=문쪽)
2. △: 핸드레일
1: Ø38 S'ST PIPE 손잡이 난간
2: 10X60 평철난간
3. ○: 벽체리스트
D1: THK9.5 석고보드 2겹(양면)
(KS50x45x0.5T C-STUD)
4. 조적조에 문창 설치시 인방설치
(인방높이는 OPEN쪽 1,800이상은
H-300, 1,800미만은 H-200 쪽은
조적쪽과 동일)
5. 보크기, 스라브두께, 벽두께,
OPENING 등은 구조도면을
우선으로 한다.
6.

실변조	천정고
SL레벨	FL레벨
7. 60: 60분 방화문
8. E: 승강기용 방화문

△				
△				
△				
△				
△				
△				
No.	Date	Revision	Description	Chkd.

(주)해인건축사사무소
HAEIN ARCHITECTURE

E-mail : sr5585@naver.com
TEL.031)987-5585, FAX.031)985-5585

도면명 TITLE

3 층 평 면 도

축 치 SCALE	A1	1 / 125
	A3	1 / 250

일 자
DATE

설 계
ARCHITECT



답 당
DRAW

검 토
CHECK

승 인
APPROVED

도면번호
DRAWING NO

A - 204

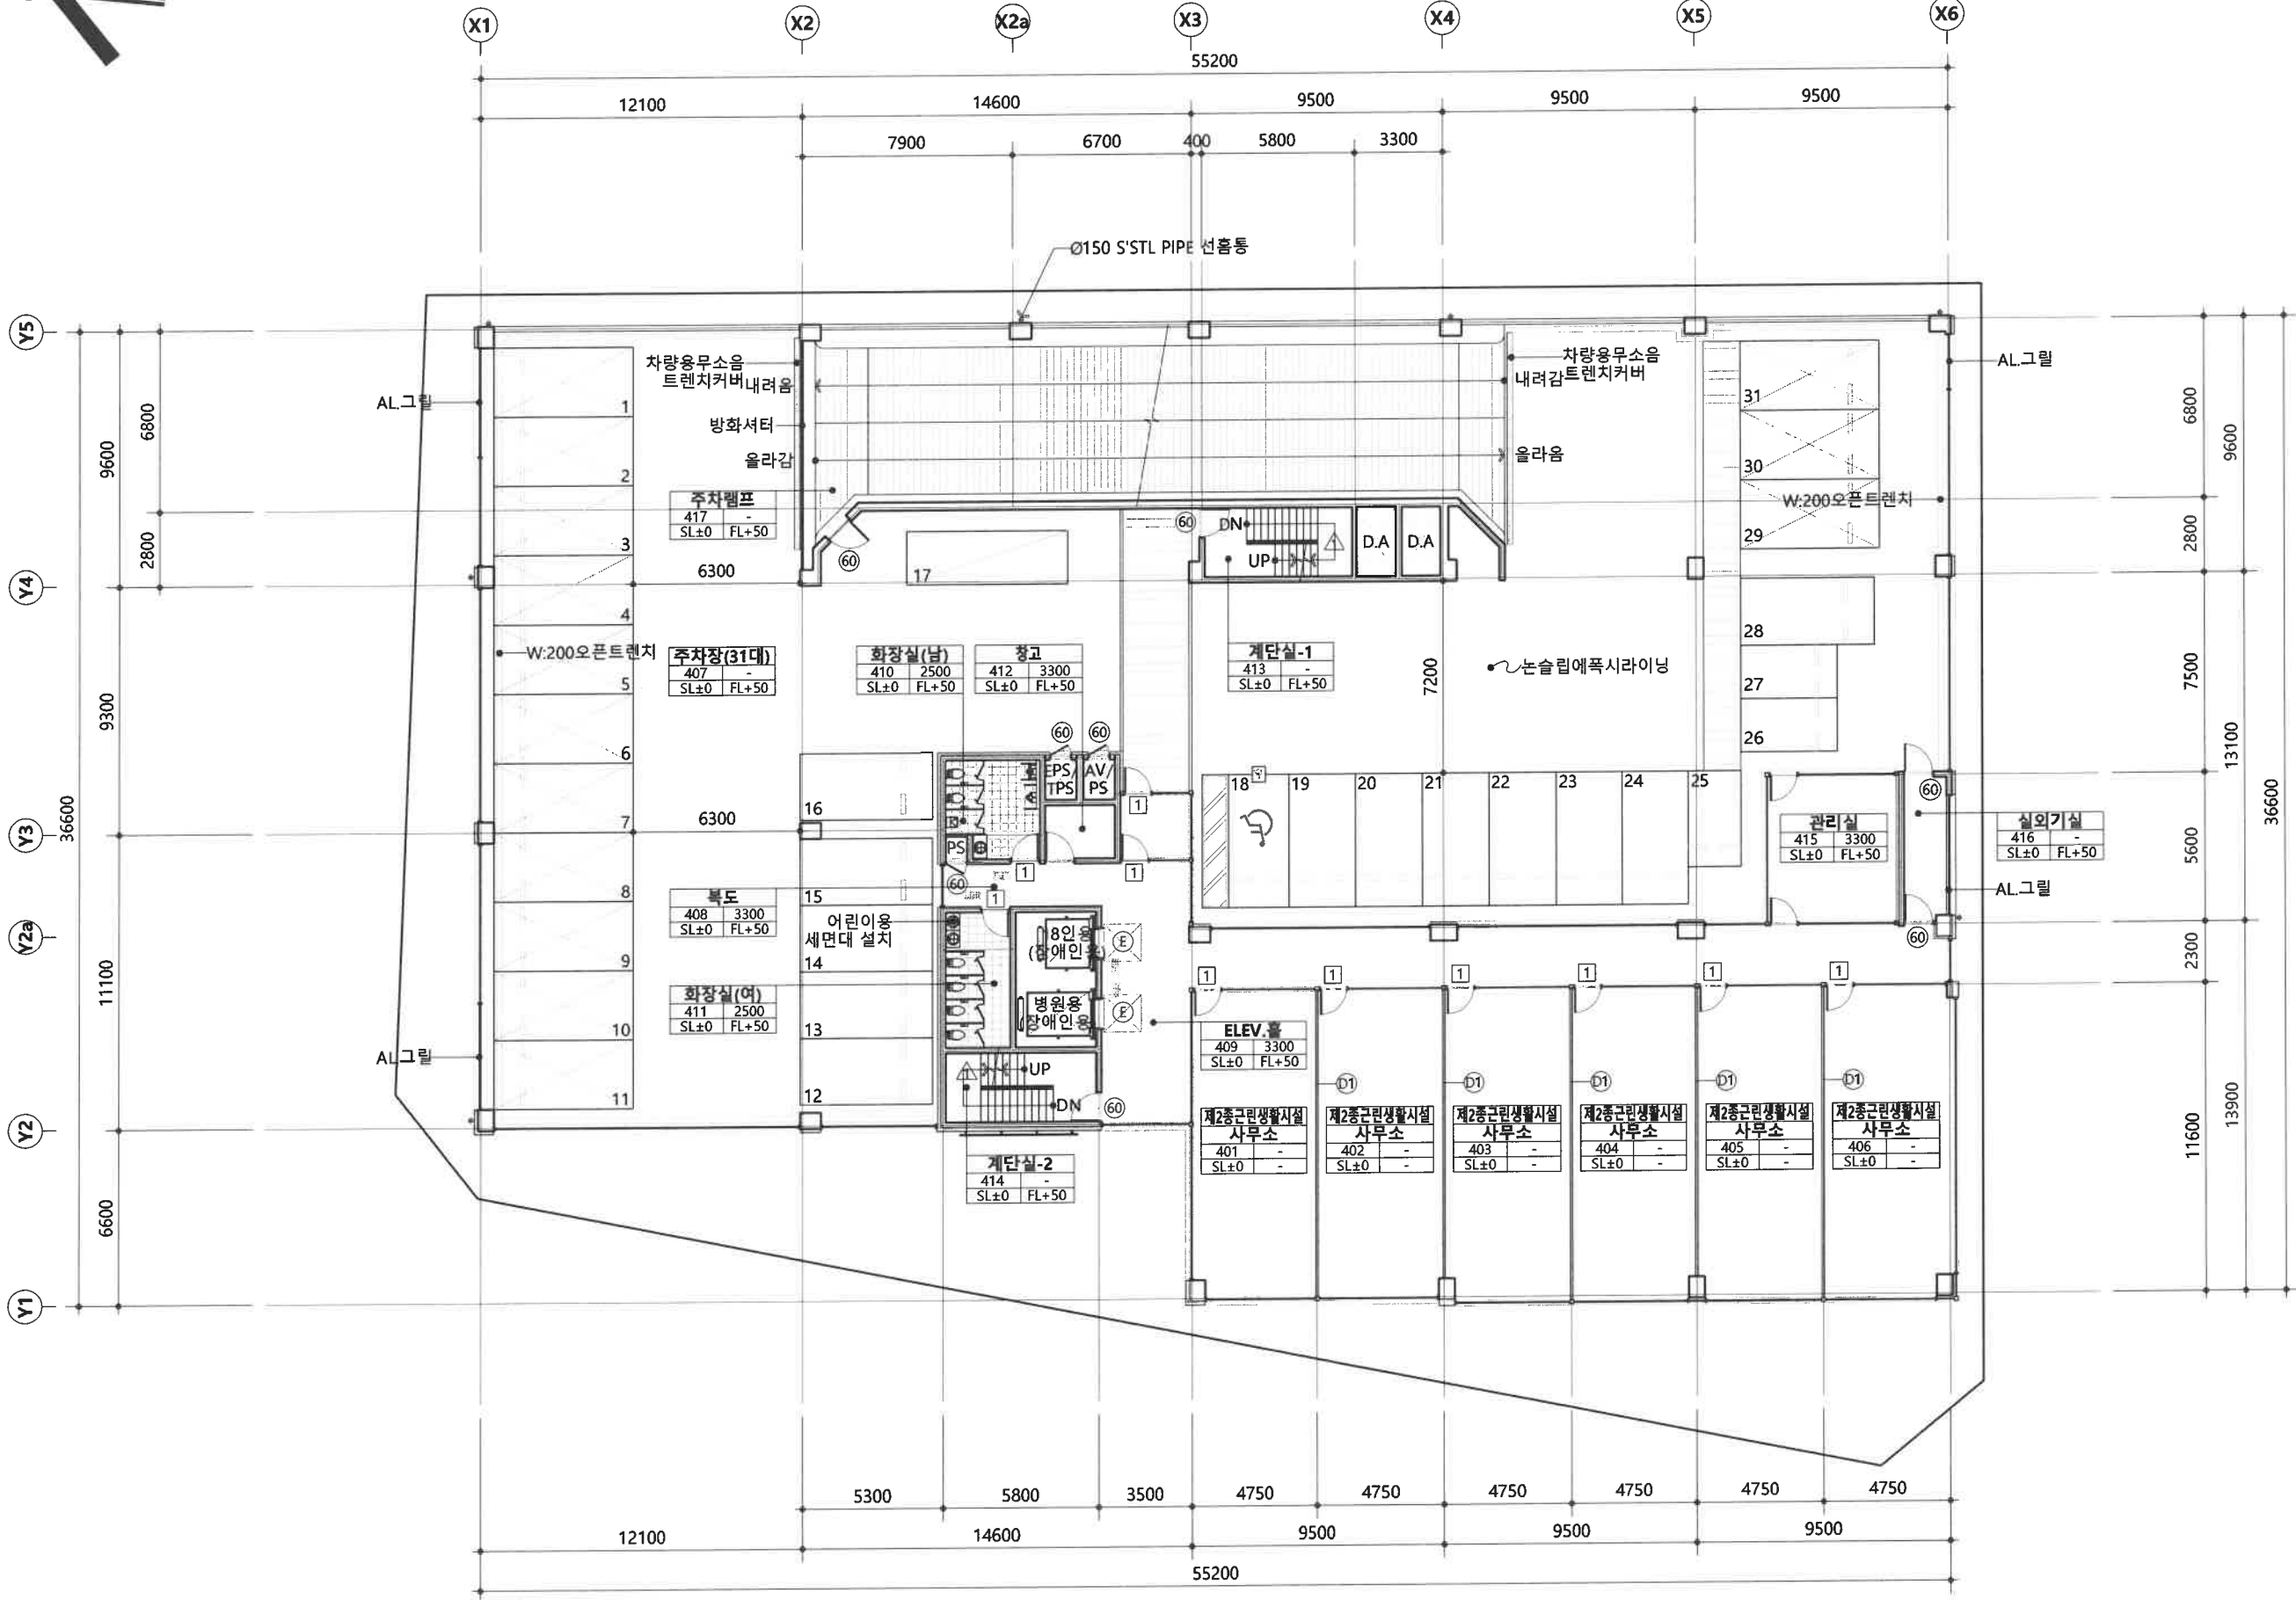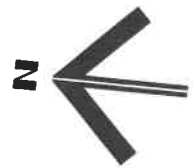

1
A

4 층 평 면 도

SCALE : 1/250

공 사 명
PROJECT TITLE

인천광역시 서구
당하동 1250번지
주차전용건축물
신축공사

- 주 기
NOTE
1. □:재료분리대
1:T-1.2 스테인레스(꼭=문쪽)
 2. △:핸드레일
1:Ø38 S'ST PIPE 손잡이 난간
2:10X60 평철난간
 3. ○:벽체리스트
D1: THK9.5 석고보드 2겹(양면)
(KS50x45x0.5T C-STUD)
 4. 조적조에 문창 설치시 인방설치
(인방높이는 OPEN쪽 1,800이상은
H-300, 1,800미만은 H-200 쪽은
조적쪽과 동일)
 5. 보크기, 스라브두께, 벽두께,
OPENING 등은 구조도면을
우선으로한다.
 6. **실명**
실면준 천정고
SL레벨 FL레벨
 7. 60: 60분 방화문
 8. 60: 승강기용 방화문

△				
△				
△				
△				
△				
△				

No.	Date	Revision	Description	Chkd.
-----	------	----------	-------------	-------

(주)해인건축사사무소
HAEIN ARCHITECTURE

E-mail : sr5585@naver.com
TEL:031)987-5585, FAX:031)985-5585

도면명 TITLE

4 층 평 면 도

축척 SCALE	A1	1 / 125
	A3	1 / 250

일 자
DATE

설 계
ARCHITECT


담 당
DRAW.

검 토
CHECK

승 인
APPROVED


도면번호
DRAWING NO

A - 205

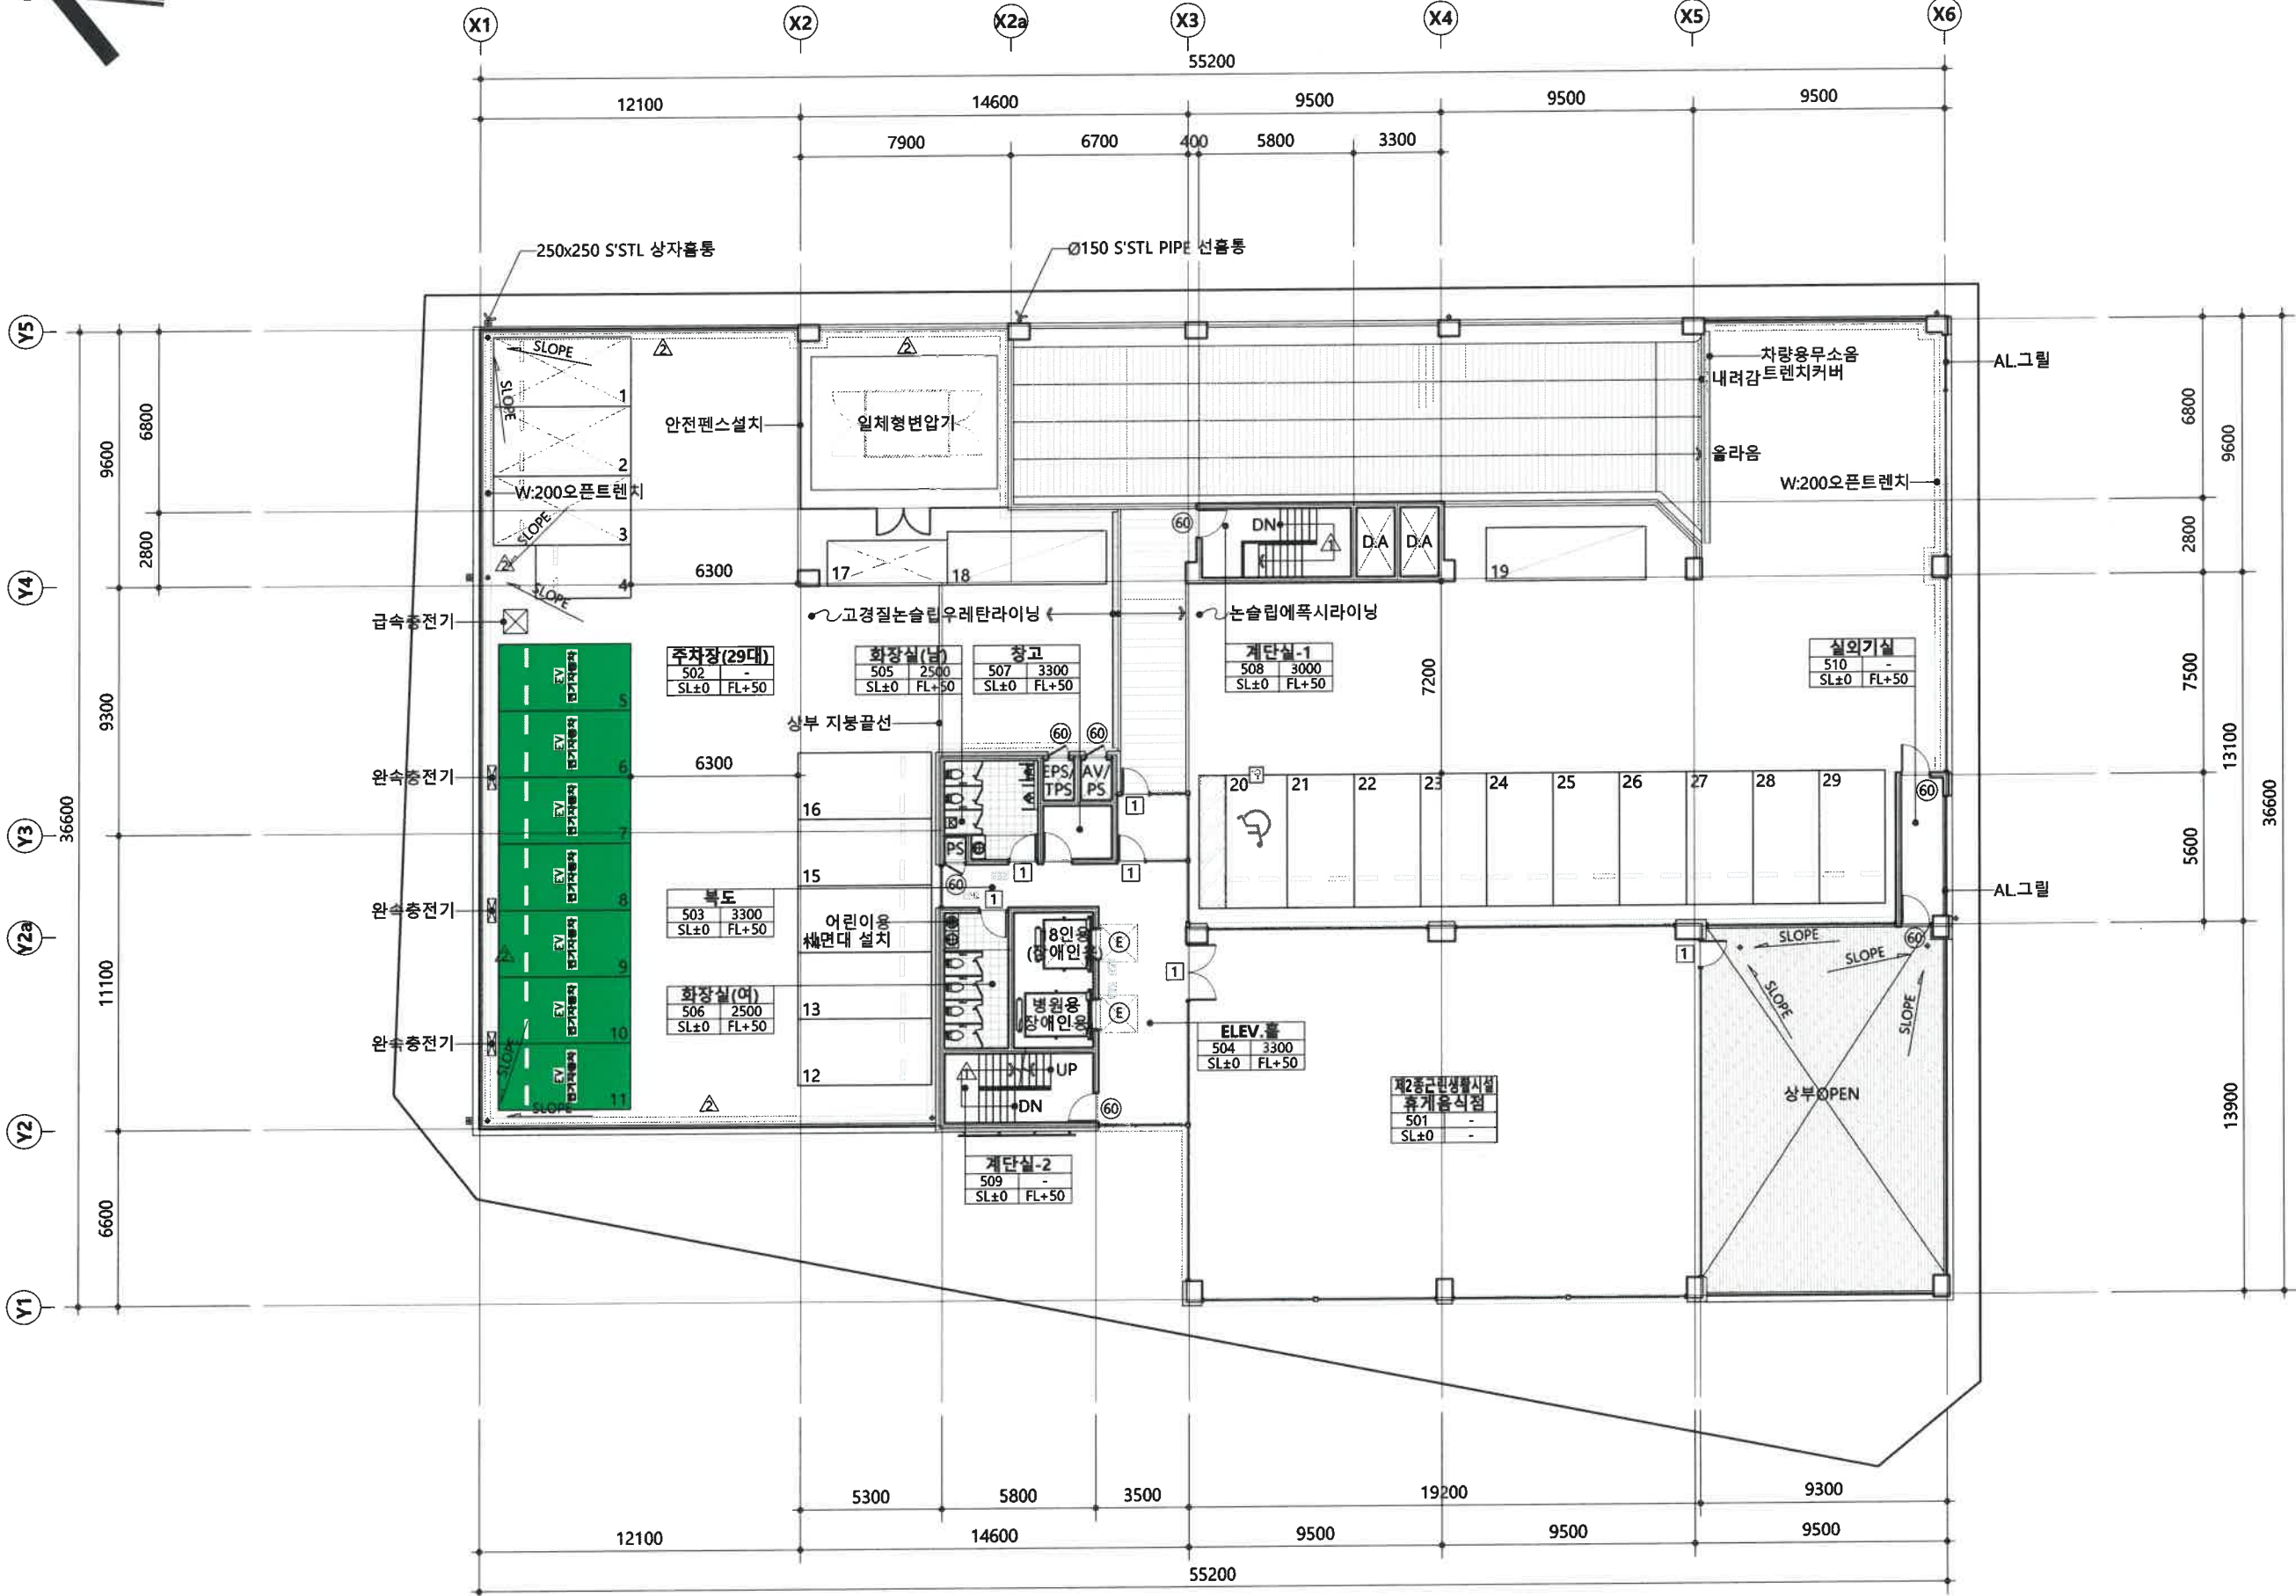

SCALE : 1/250

A - 206

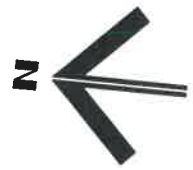

1
A 지붕층 평면도
SCALE : 1/250

공사명
PROJECT TITLE

인천광역시 서구
당하동 1250번지
주차전용건축물
신축공사

주 기
NOTE

1. □: 재료분리대
1: T-1.2 스테인레스(꼭=문쪽)
2. △: 핸드레일
1: Ø38 S'ST PIPE 손잡이 난간
2: 10X60 평철난간
3. ○: 벽체리스트
D1: THK9.5 석고보드 2겹(양면)
(KS50x45x0.5T C-STUD)
4. 조적조에 문, 창 설치시 인방설치
(인방높이는 OPEN쪽 1,800이상은
H-300, 1,800미만은 H-200 혹은
조적폭과 동일)
5. 보크기, 스라브두께, 벽두께,
OPENING 등은 구조도면을
우선으로한다.
6.

실명
실명중 천정고
SL레벨 FL레벨
7. 60: 60분 방화문
8. ㉔: 승강기용 방화문

△			
△			
△			
△			
△			
△			

No.	Date	Revision Description	Chkd.
-----	------	----------------------	-------

(주)해인건축사사무소
HAEIN ARCHITECTURE

E-mail : sr5585@naver.com
TEL:031)987-5585, FAX:031)985-5585

도면명 TITLE

지붕층 평면도

축척 SCALE	A1	1 / 125
	A3	1 / 250

일 자
DATE

설 계
ARCHITECT



담 당
DRAW.

검 토
CHECK

승 인
APPROVED

도면번호
DRAWING NO

A - 207

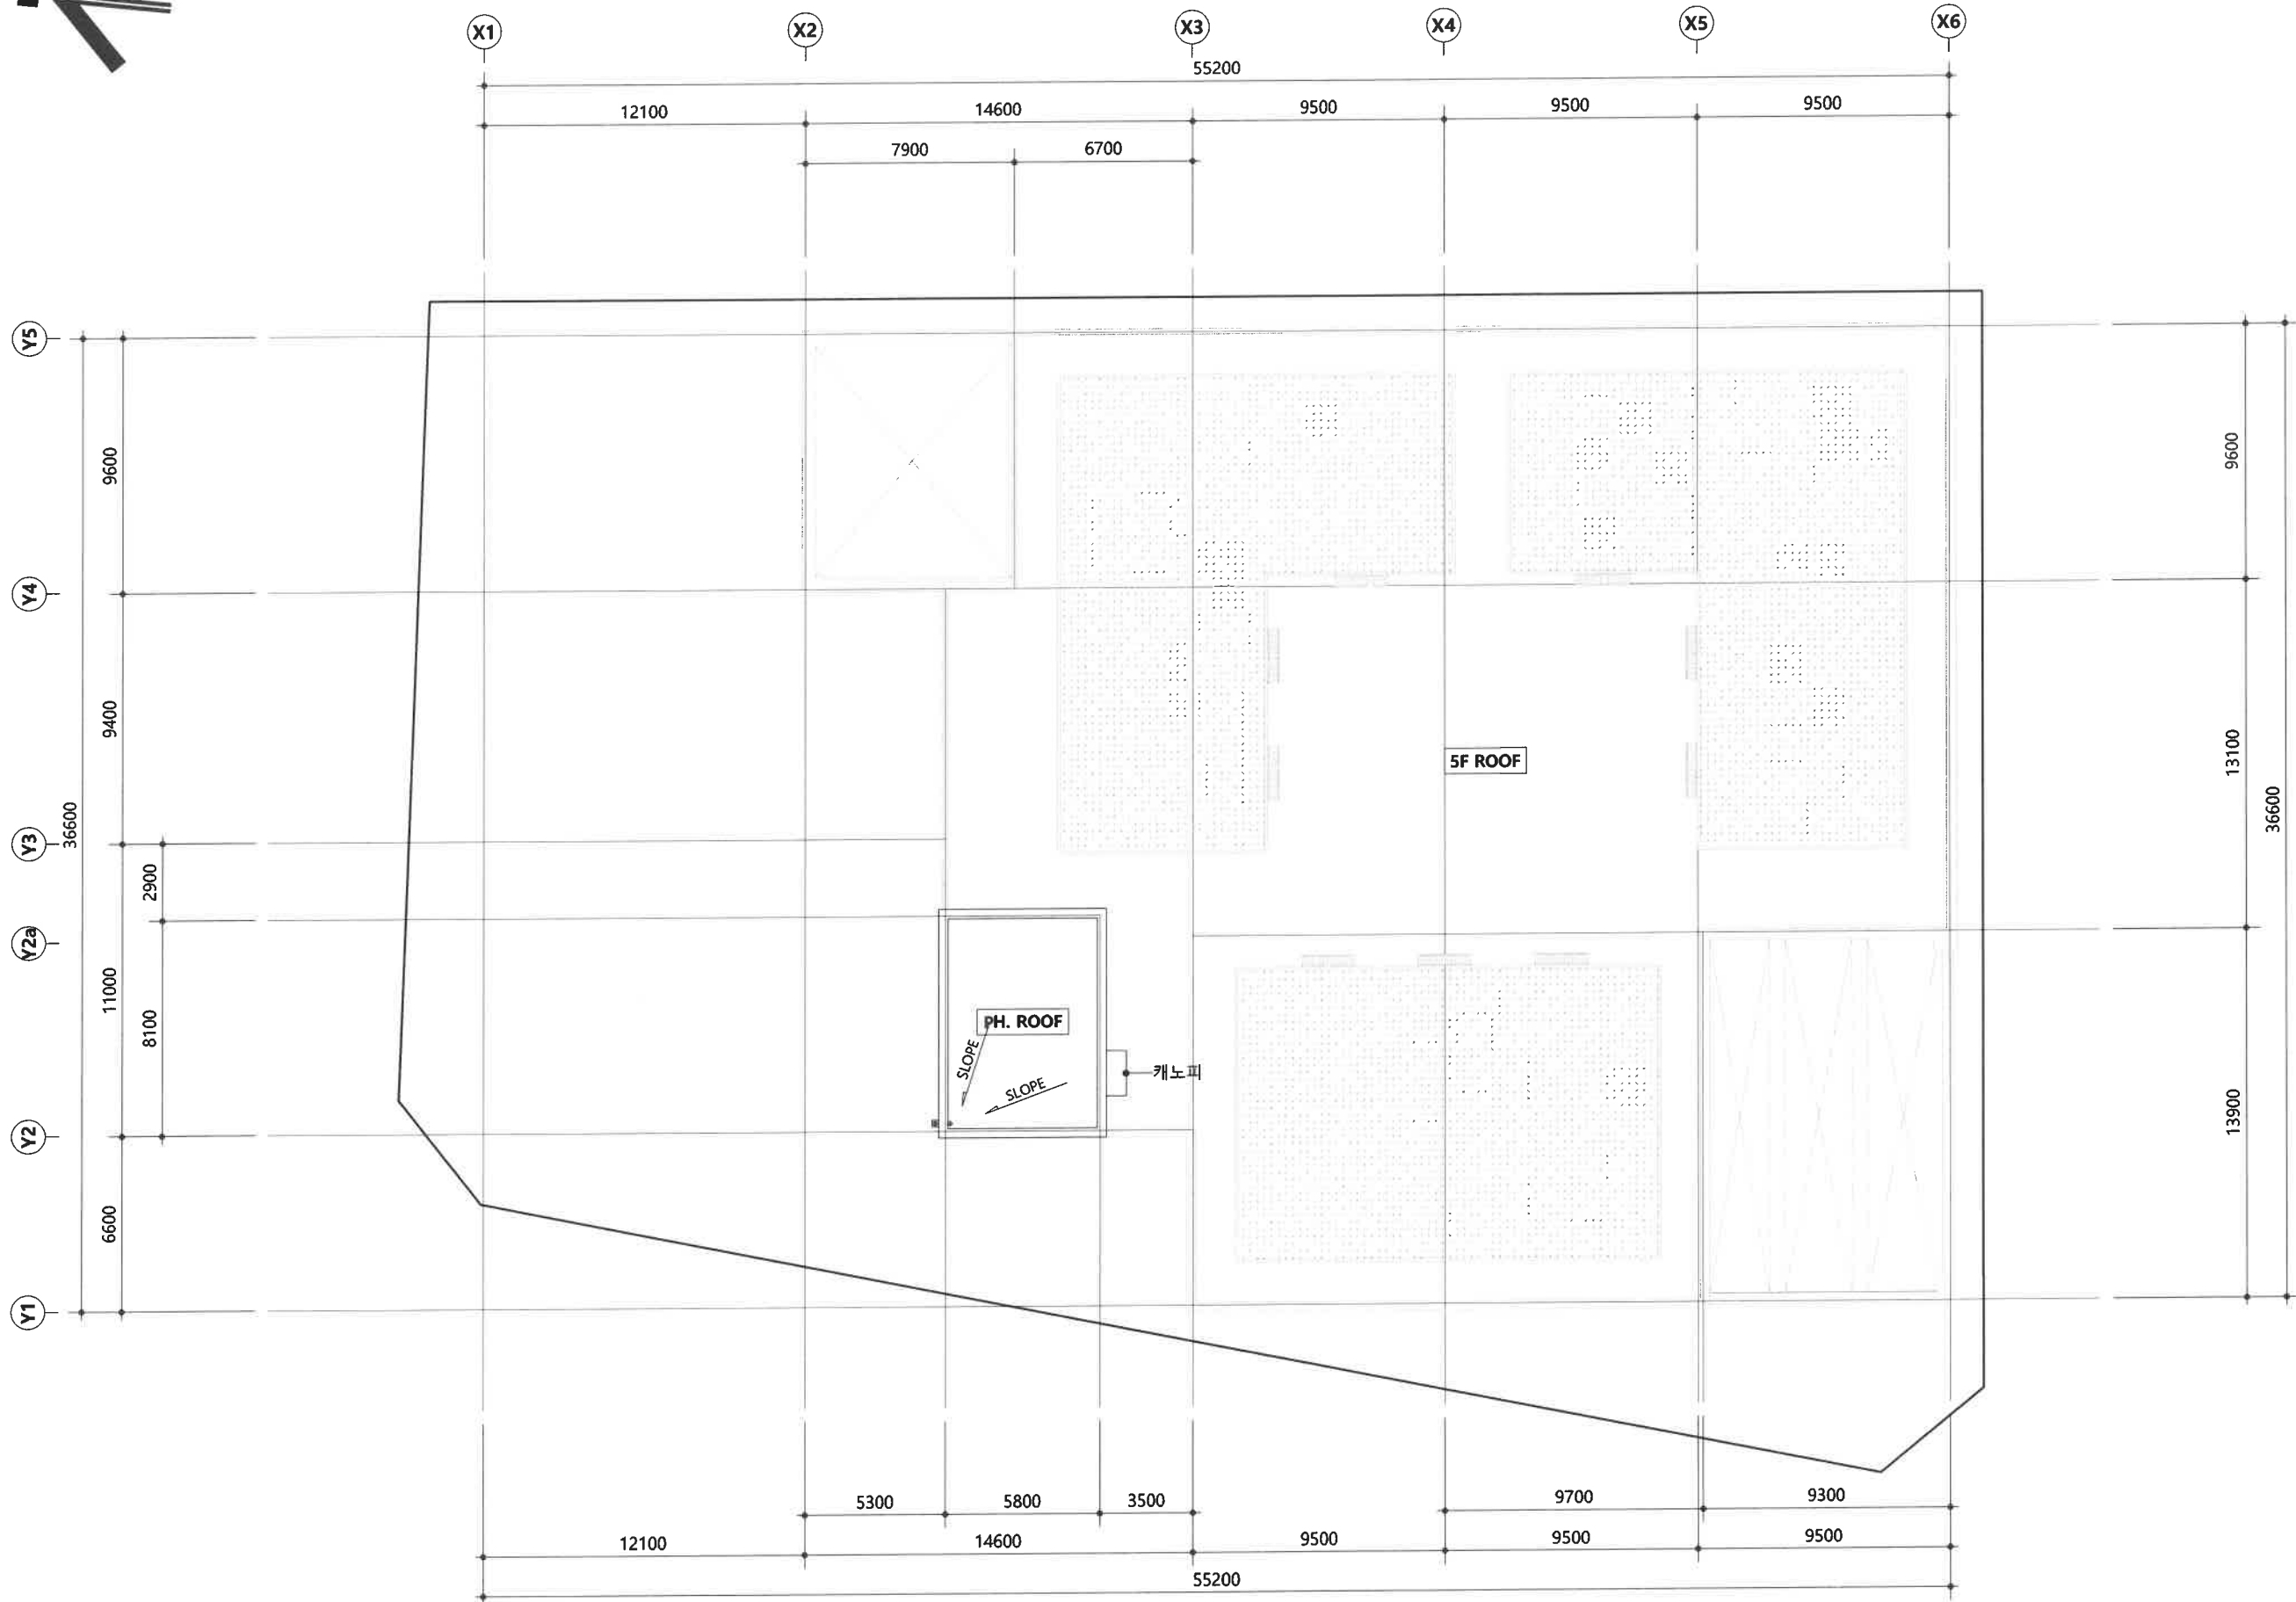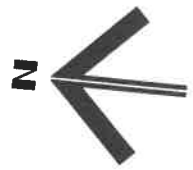

1
A

옥탑지붕 평면도

SCALE : 1/250

공 사 명
PROJECT TITLE

인천광역시 서구
당하동 1250번지
주차전용건축물
신축공사

주 기
NOTE

1. □ : 재료분리대
1: T-1.2 스테인레스(폭=문폭)
2. △ : 핸드레일
1: Ø38 S'T PIPE 손잡이 난간
2: 10X60 평철난간
3. ○ : 벽체리스트
D1 : THK9.5 석고보드 2겹(양면)
(K550x45x0.5T C-STUD)
4. 조적조에 문, 창 설치시 인방설치
(인방높이는 OPEN폭 1,800이상은
H-300, 1,800미만은 H-200 혹은
조적폭과 동일)
5. 보크기, 스라브두께, 벽두께,
OPENING 등은 구조도면들
우선으로한다.
6. 실 명
실번호 전정고
SL레벨 FL레벨
7. 60 : 60분 방화문
8. ㉔ : 승강기용 방화문

△				
△				
△				
△				
△				
△				

No.	Date	Revision	Description	Chkd.
-----	------	----------	-------------	-------

(주)해인건축사사무소
HAEIN ARCHITECTURE

E-mail : sr5585@naver.com
TEL:031)987-5585, FAX:031)985-5585

도면명 TITLE

옥탑지붕 평면도

축척 SCALE	A1	1 / 125
	A3	1 / 250

일 자
DATE

설 계
ARCHITECT

담 당
DRAW.

검 토
CHECK

승 인
APPROVED

도면번호
DRAWING NO

A - 208